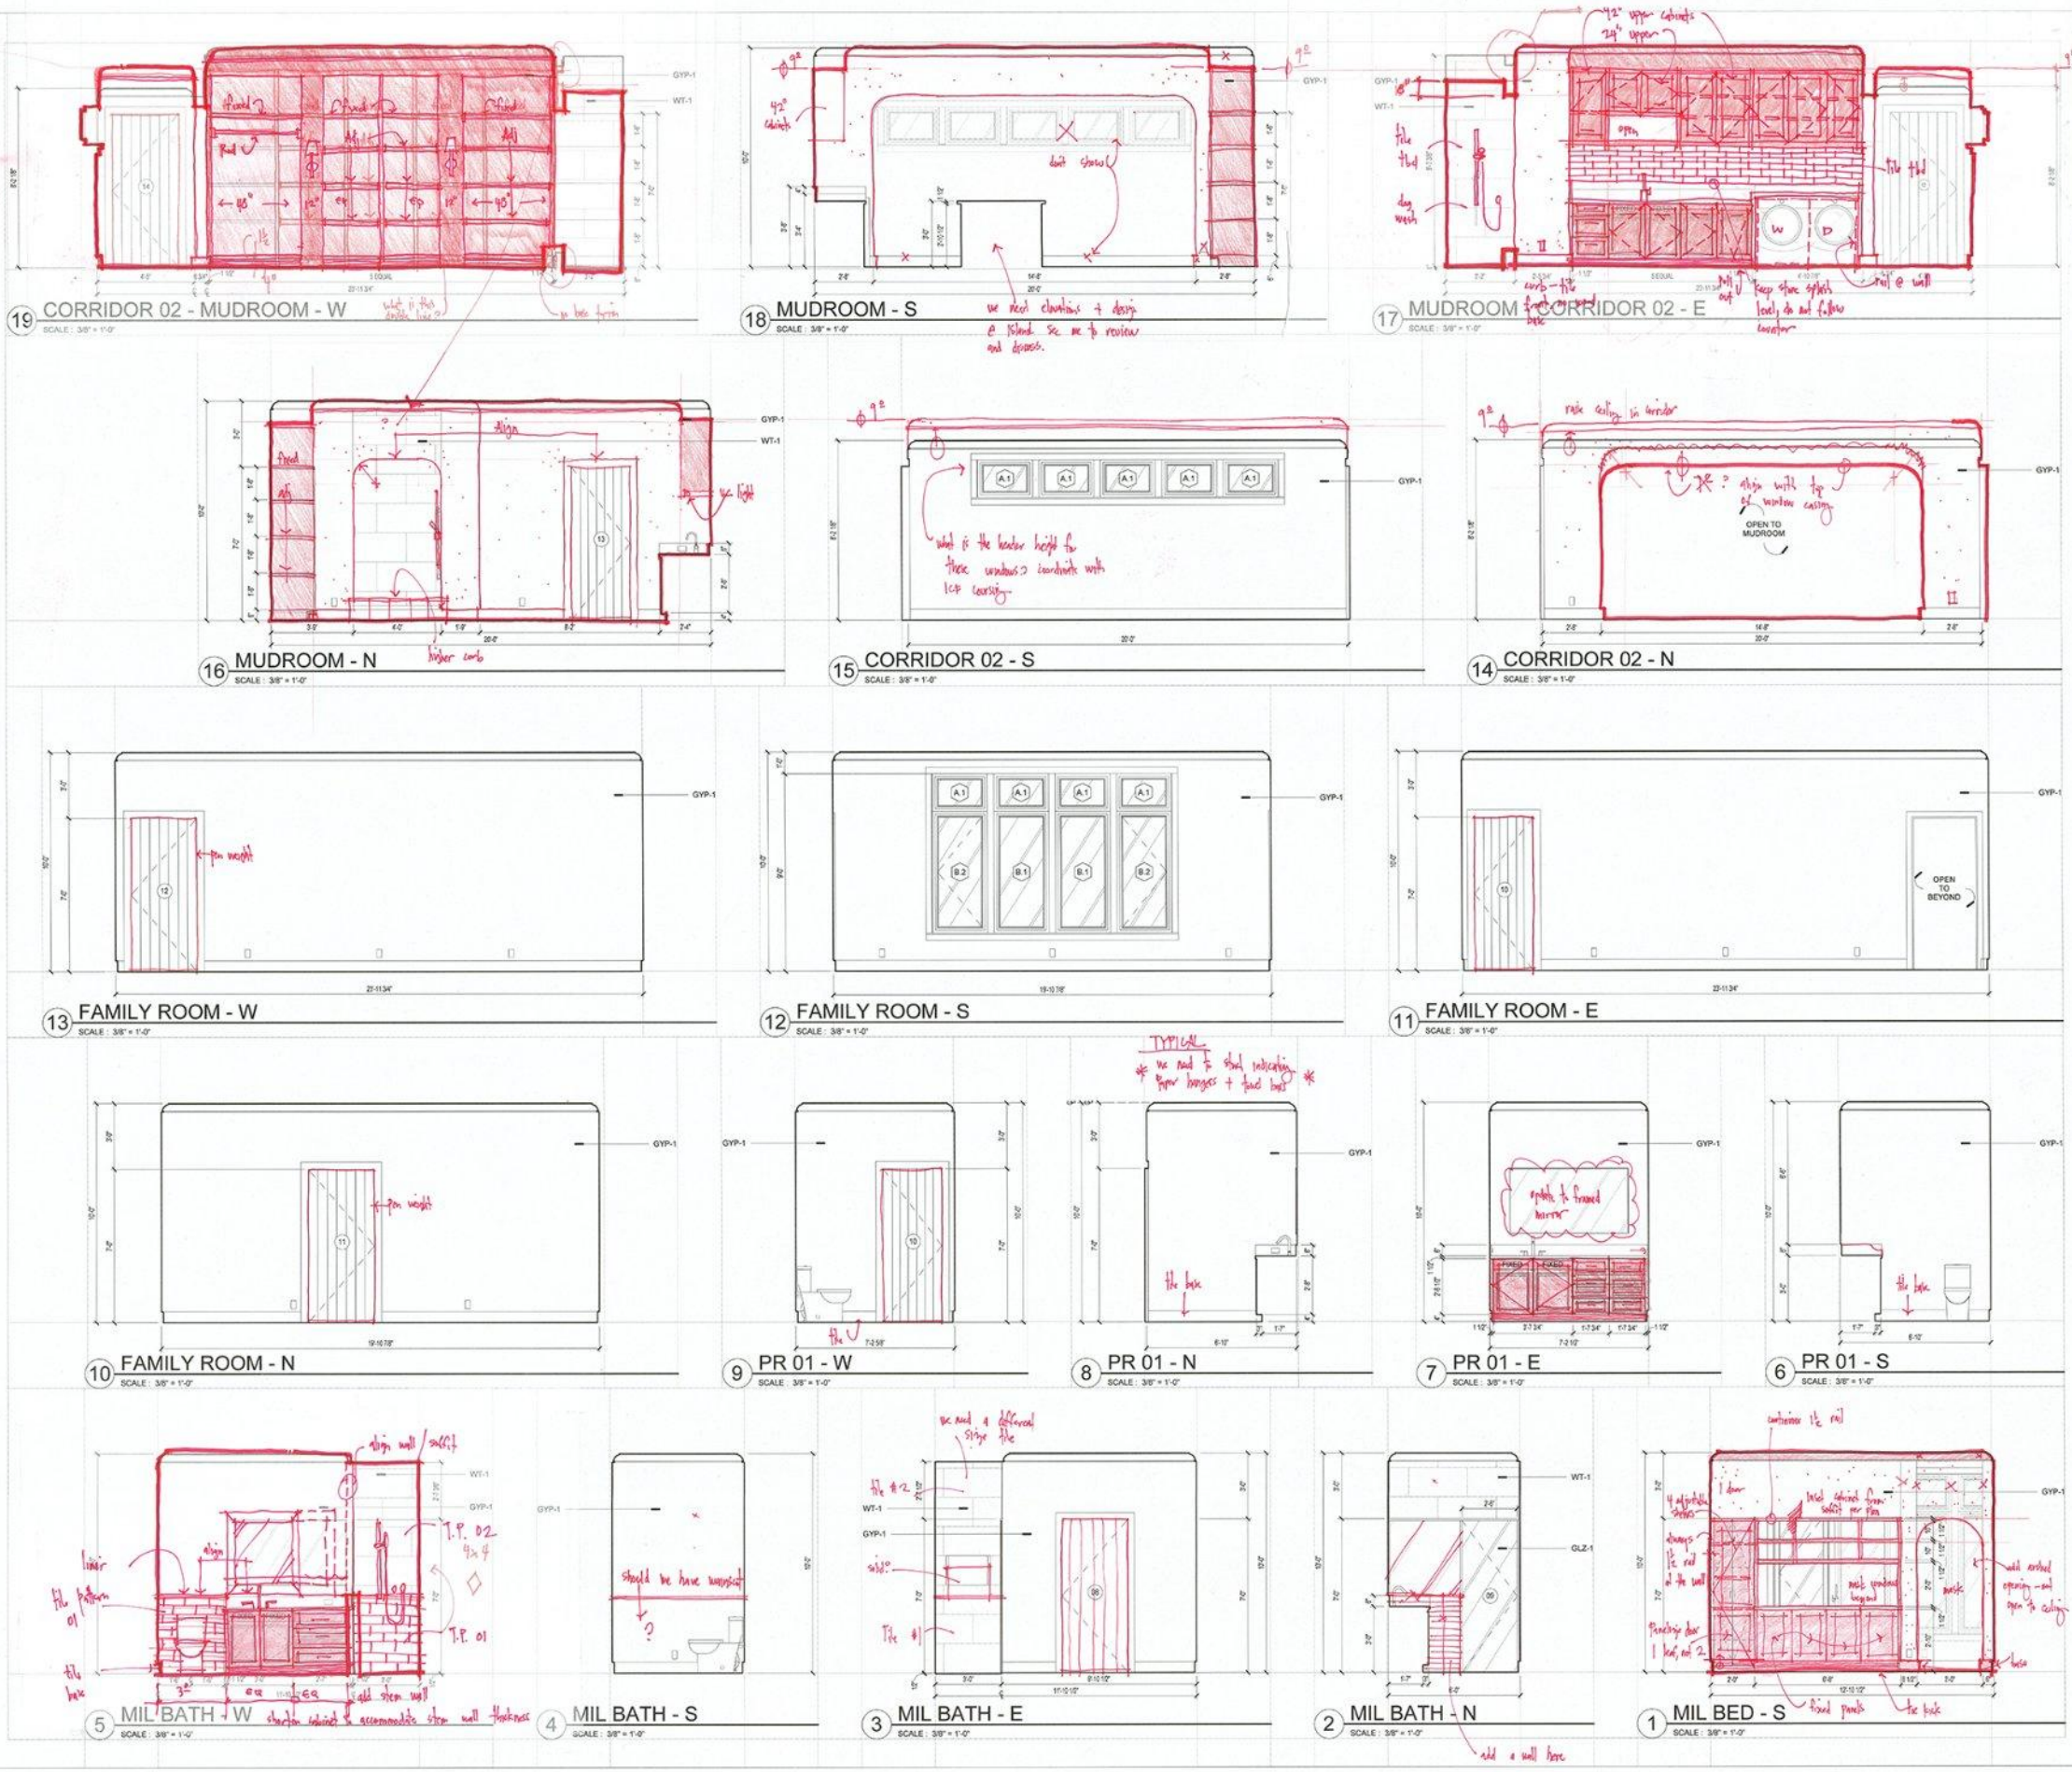

BO KA Powell

architecture | interiors | planning | graphics
8070 Park Lane, Ste. 300 | Dallas, Texas 75231
Tel 972.701.9000 | Fax 972.991.3008
www.bokapowell.com

These documents are issued for pricing only and are not for regulatory approval, permitting or construction.

Arch: Donald R. Powell, Jr. Reg. No.: 7206
Arch: Chris W. Barnes Reg. No.: 10147
Arch: John E. Orfield Reg. No.: 11164
Arch: R. Andrew Bennett Reg. No.: 18129

CLIENT

GENERAL CONTRACTOR

STRUCTURAL ENGINEER

MEP ENGINEER

project

The drawings and written material herein constitute original work of the architect, and as intellectual property and instruments of service, are subject to copyright and may not be reproduced, distributed, published or used in any way without the express written consent of the architect.

original issue

revisions

title

INTERIOR ELEVATIONS

project number

date

sheet

A732